



PRELIMINARY, NOT FOR FABRICATION

CanalRung · github.com/BoujeeEnjinia1701/canalrung


REV	DESCRIPTION	DATE	BY
P1	Preliminary GA for TRL 3 (from cad/src/model.py)	2026-10-03	AC
P2	CNR-DDR-002: design for construction	2026-10-03	AC
P3	CNR-DDR-003: 9 mm ropes; 500 x 1,200 footing standard	2026-10-03	AC

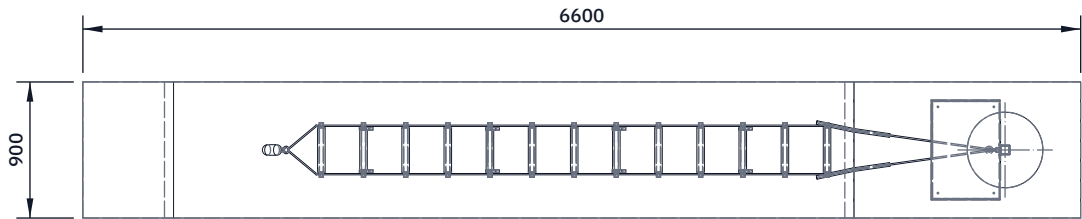


TOP VIEW
Scale 1:50; looking down (along -Z)

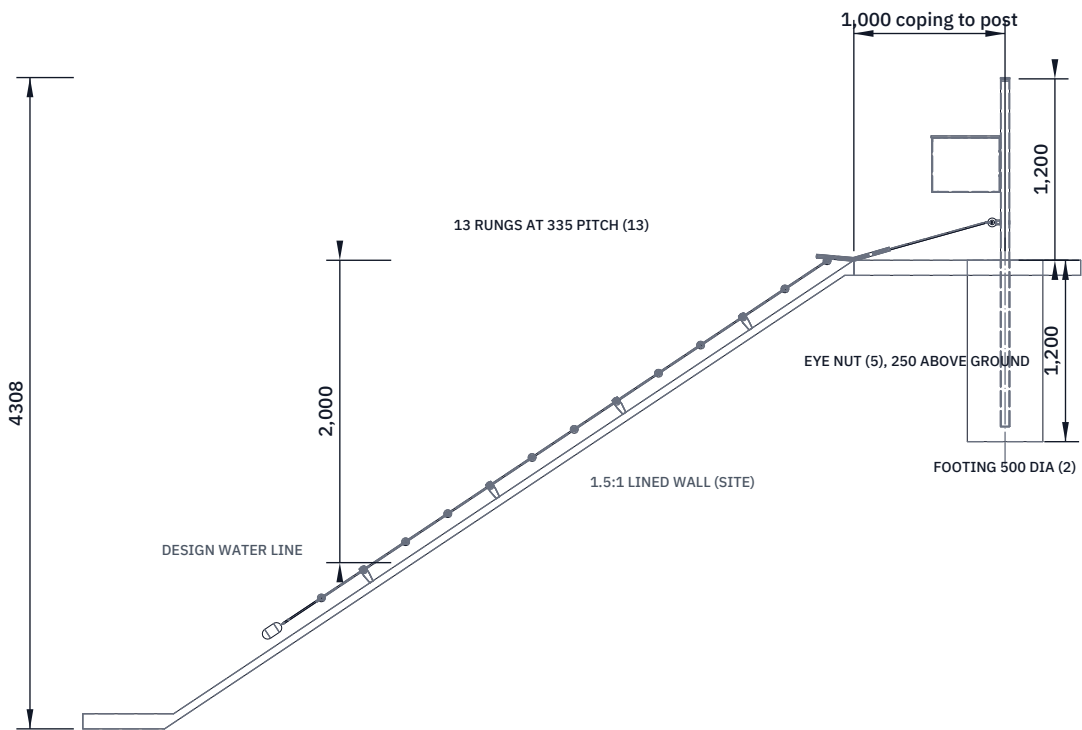

FRONT VIEW
Scale 1:50; looking at the front (along +Y)

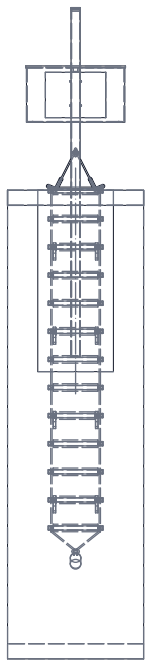

RIGHT VIEW
Scale 1:50; looking at the right side (along -X)

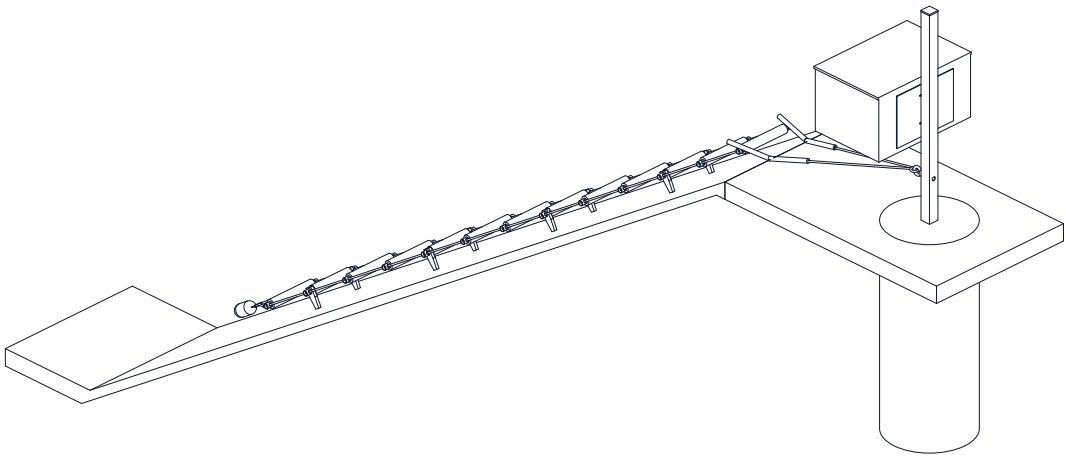

ISOMETRIC VIEW
Not to scale; seen from the bank side, front right and above; grey wall is the site

MAIN DIMENSIONS AND INTERFACES (MM)

- Post 60 x 60 x 3 SHS x 2,300; 1,100 in a 500 x 1,200 footing
- Post centre 1,000 back from the coping; top 1,200 above ground
- Anchor: M16 forged eye nut on an M16 x 90 bolt, 250 above ground
- Box about 450 x 650 x 360, base 450 up; 2 square U-bolts M8
- Ladder: 13 rungs, 335 pitch, ropes 320 apart; section 4,020
- Rung 28.6 x 1.65 Al tube x 360; foam float sleeve 50 OD
- Stand-offs on rungs 3, 6, 9, 12: rung axis 95 off the wall
- Ropes 9 kernmantle, about 8.0 m each; knot under every rung end
- Ladder as thrown about 4.3 kg; soft 0.5 kg throw weight
- Small parts (bushes, caps, knots, seizings): DWG-106, 109
- Third-angle; front view from -Y; canal along Y; (n) = BOM line

CANALRUNG

github.com/BoujeeEnjinia1701/canalrung

Throwable canal ladder and bank station: general arrangement

DRAWING NO. CNR-DWG-001			REV P3	SHEET 1 of 1	SIZE ANSI B
SCALE 1:50	UNITS mm	PROJECTION 	DATE 2026-10-03		DRAWN Amish Chadha
MATERIAL / NOTES Steel post, aluminium rungs, kernmantle rope; see bom/bom.csv. PRELIMINARY, NOT FOR FABRICATION					
Licensed CERN-OHL-S-2.0 · Design Molecule Lab · designmolecule.com				Generated from cad/src; do not edit by hand	