


CONCEPT, NOT FOR FABRICATION


CanalRung · github.com/BoujeeEnjinia1701/canalrung

REV	DESCRIPTION	DATE	BY
P1	Concept sheet from the constructable model	2026-10-03	AC
P2	CNR-DDR-003: 9 mm ropes; 500 x 1,200 footing	2026-10-03	AC

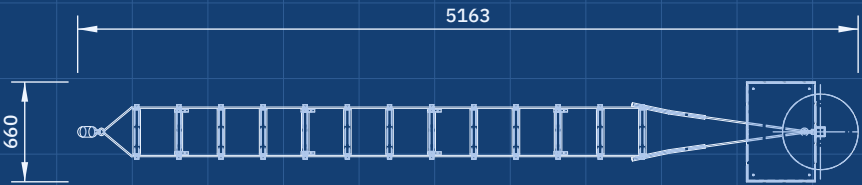


TOP VIEW

Scale 1:50; looking down (along -Z)

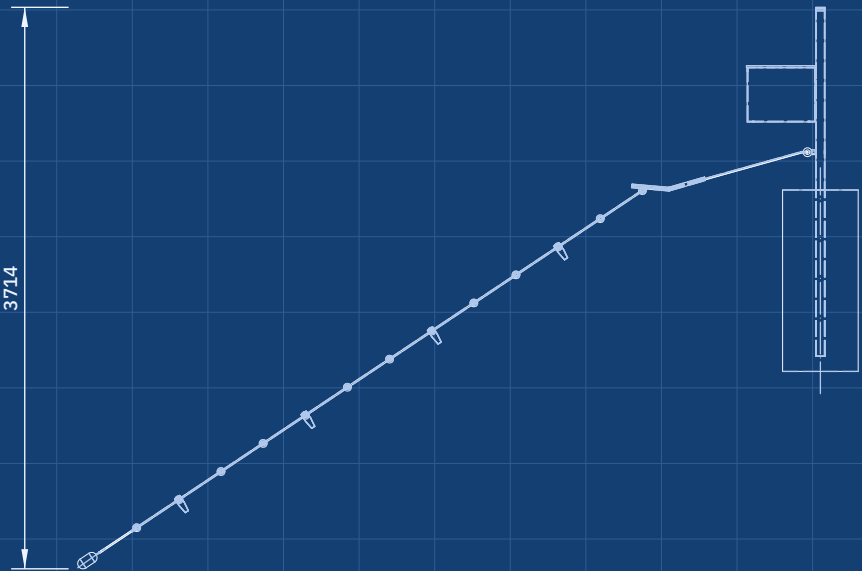


FRONT VIEW

Scale 1:50; looking at the front (along +Y)

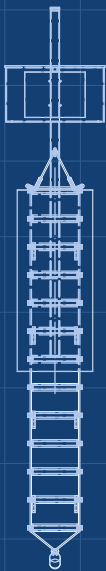

RIGHT VIEW

Scale 1:50; looking at the right side (along -X)

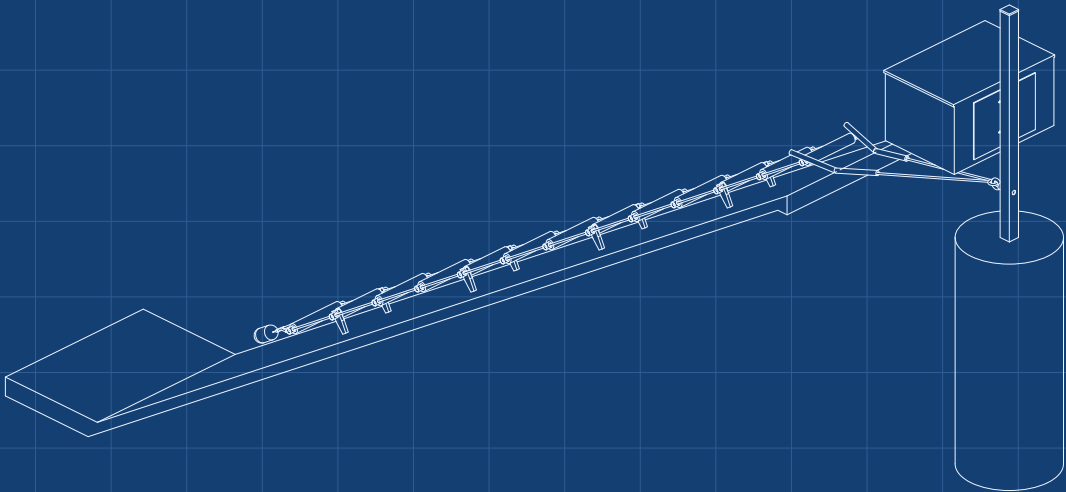

ISOMETRIC VIEW

Not to scale; seen from the bank side, front right and above; grey is the site

KEY FIGURES

- 13 floating rungs at 335 mm pitch; 4.02 m rung section
- Reaches water 2.1 m down a 1.5:1 wall, 3.8 m down a vertical wall
- Each rung floats with 0.22 to 0.28 kg to spare; soft 0.5 kg throw weight
- Rung: 0.56 of yield at 1.5 kN; 9 mm ropes 18.4 kN wet with knots
- Anchor eye nut on a post in a 500 x 1,200 footing; 4.5 kN target
- Ladder as thrown 4.3 kg (4.5 kg target); about 15 s to deploy (est.)
- Never enter the water: throw, anchor and call for help

CANALRUNG

github.com/BoujeeEnjinia1701/canalrung

Throwable floating canal ladder and bank station

DRAWING NO. CNR-DWG-010		REV P2	SHEET 1 of 1	SIZE ANSI B
SCALE 1:50	UNITS mm	PROJECTION 	DATE 2026-10-03	DRAWN Amish Chadha

MATERIAL / NOTES
Massing model for concept communication