BUILD PLAN SKETCH, PLAN NOT YET BUILT

CanalRung · github.com/BoujeeEnjinia1701/canalrung

REV	DESCRIPTION	DATE	BY
P1	Making sketch for the prototype build plan	2026-10-03	AC

TOP VIEW

Scale 1:20; looking down (along -Z)

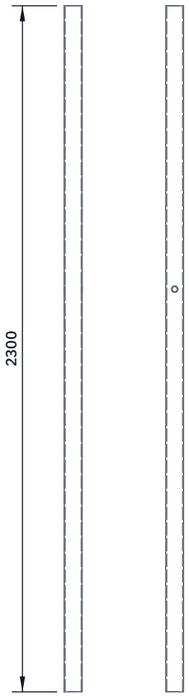

FRONT VIEW

Scale 1:20; looking at the front (along +Y)

RIGHT VIEW

Scale 1:20; looking at the right side (along -X)

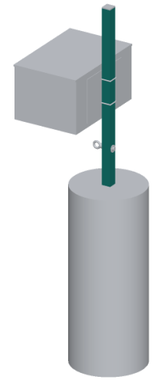

WHERE IT GOES

This part in colour, its neighbours in grey

HOW TO MAKE IT AND HOW IT FITS

Cut 2,300 long, square; file the burr off both ends.
Mark one face as the canal side. 1,350 up from the bottom end
(250 above ground when set), on the face centre line:
canal-side wall: drill 17.5 for the M16 bolt;
back wall, same axis: drill 21.5 for the crush tube.
Use a drill guide or drill press so both holes share one axis.
Deburr; cold galvanising paint on the holes and cut ends.
Mark a ground line 1,100 up from the bottom end.
Fits: 1,100 sits in the footing, 100 above its base;
plate and box on the canal face; cap on top.

CANALRUNG

github.com/BoujeeEnjinia1701/canalrung

Post: making sketch

DRAWING NO.	REV	SHEET	SIZE
CNR-DWG-101	P1	1 of 1	ANSI B

SCALE	UNITS	PROJECTION	DATE	DRAWN
1:20	mm		2026-10-03	Amish Chadha

MATERIAL / NOTES

Hot-dip galvanised steel 60 x 60 x 3 SHS, S235 or better

Licensed CERN-OHL-S-2.0 · Design Molecule Lab · designmolecule.com

Generated from cad/src; do not edit by hand